

NM Group
A TRIMBLE COMPANY

Network Mapping Inc.
6880 S.McCarren Blvd.
Ste 11
Reno NV 89509
+1 7757374537

North Litchfield - Tewksbury



nationalgrid



A3 VEGETATION CLEARANCE FIELD MAP	
Title:	
Circuit:	O215
Circuit Name:	North Litchfield - Tewksbury
Sheet Number:	Sheet 4 of 125
Project Ref.:	NMIP17053
Coord. System:	UTM - NAD83
Zone:	19 N
Units:	US Feet
Survey Date:	May 2017
Version:	1.0
Published Date:	12/09/2017
Client:	National Grid

Legend	
Conductor Left	
Conductor Centre	
Conductor Right	
Shield Wire	
Right of Way	
Tower	
Infringements 115kV lines:	Infringements 200+kV lines:
Within 5ft	Within 15ft
Within 5ft - 10ft	Within 15ft - 20ft

ROW# _____
 Contractor _____
 Foreman Name _____
 Date Completed _____

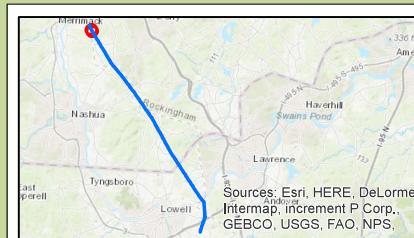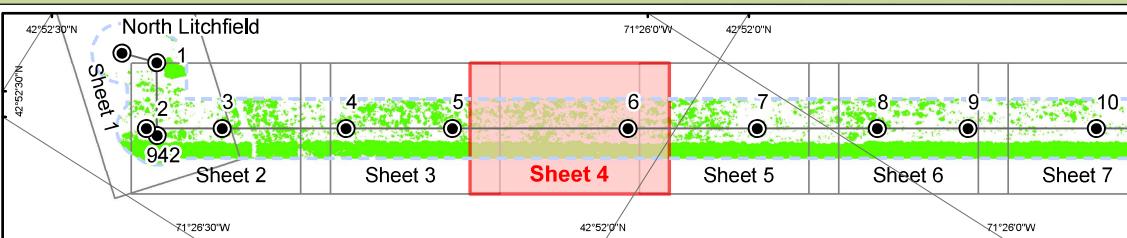



A3 VEGETATION CLEARANCE FIELD MAP	
Title:	
Circuit:	O215
Circuit Name:	North Litchfield - Tewksbury
Sheet Number:	Sheet 29 of 125
Project Ref.:	NMIP17053
Coord. System:	UTM - NAD83
Zone:	19 N
Units:	US Feet
Survey Date:	May 2017
Version:	1.0
Published Date:	12/09/2017
Client:	National Grid

Legend

- Conductor Left
- Conductor Centre
- Conductor Right
- Shield Wire
- Right of Way
- Tower

Infringements 115kV lines: Infringements 200+kV lines:



- Within 5ft
- Within 5ft - 10ft
- Within 15ft
- Within 15ft - 20ft


ROW# _____

Contractor _____

Foreman Name _____

Date Completed _____

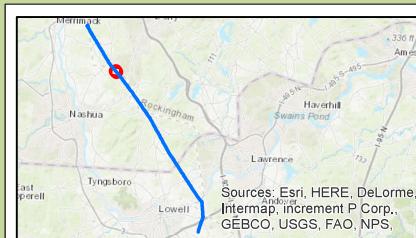
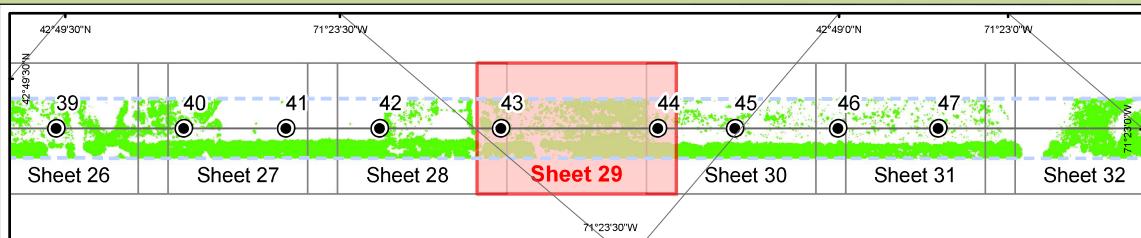


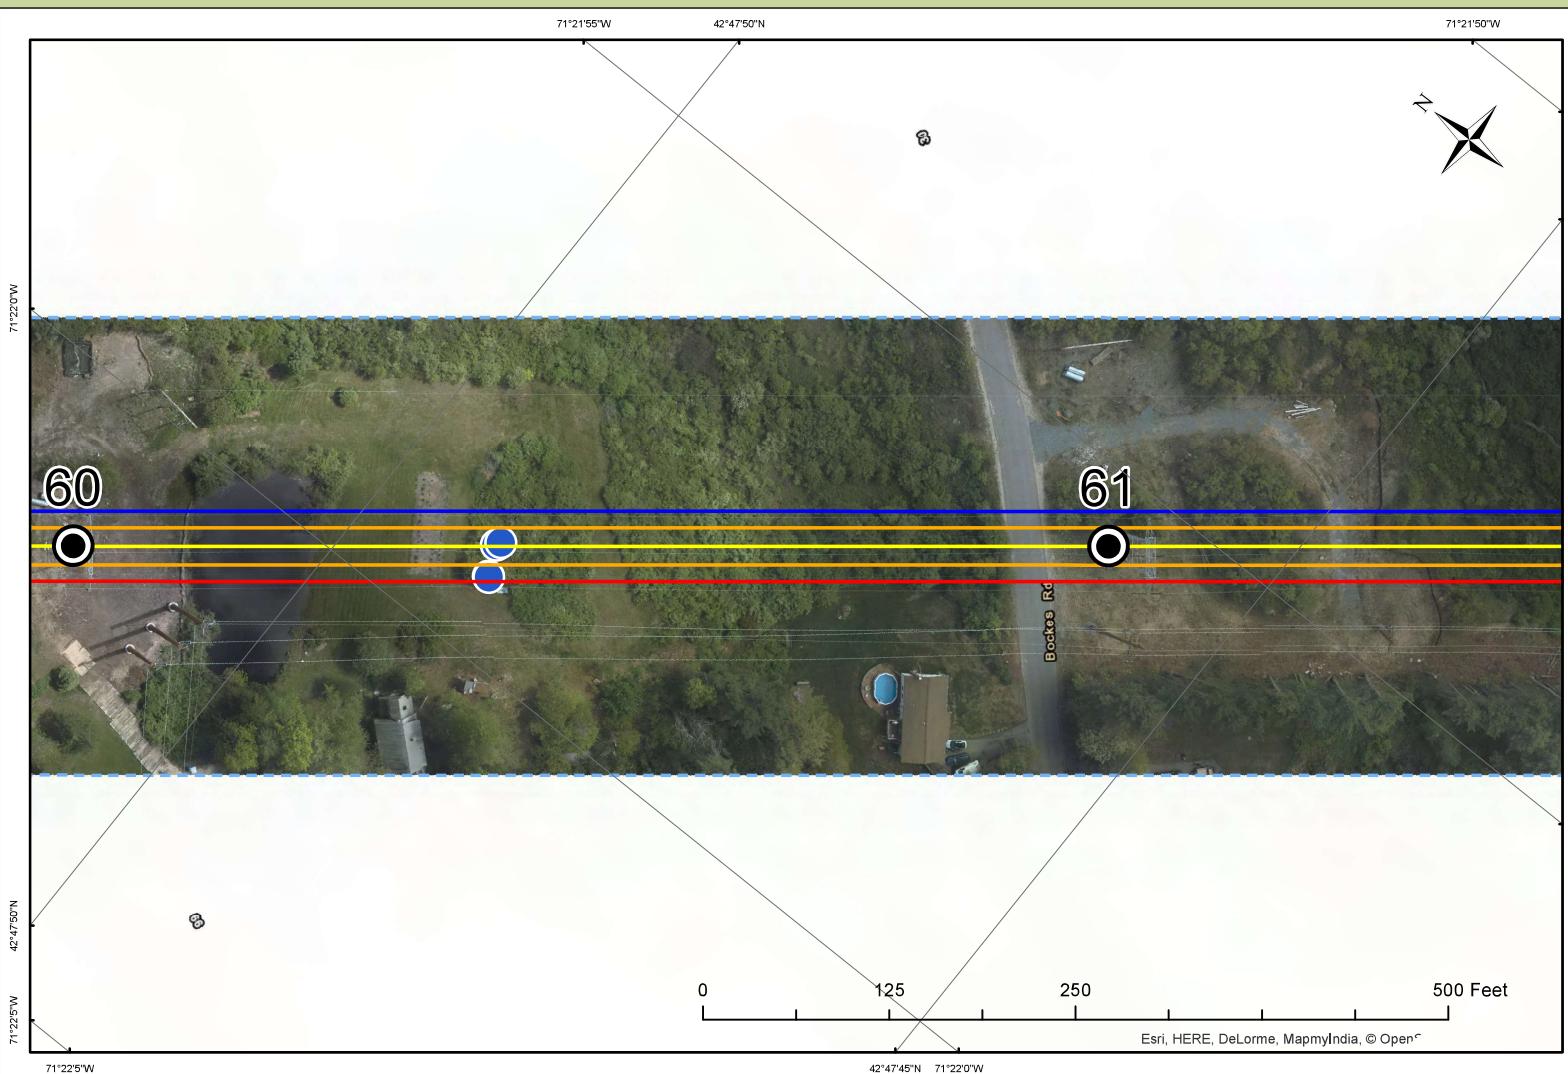


A3 VEGETATION CLEARANCE FIELD MAP	
Title:	
Circuit:	O215
Circuit Name:	North Litchfield - Tewksbury
Sheet Number:	Sheet 41 of 125
Project Ref.:	NMIP17053
Coord. System:	UTM - NAD83
Zone:	19 N
Units:	US Feet
Survey Date:	May 2017
Version:	1.0
Published Date:	12/09/2017
Client:	National Grid

Legend	
Conductor Left	(Blue line)
Conductor Centre	(Yellow line)
Conductor Right	(Red line)
Shield Wire	(Orange line)
Right of Way	(Dashed blue line)
Tower	(Black circle)
Infringements 115kV lines:	Infringements 200+kV lines:
Within 5ft (Purple dot)	Within 15ft (Dark Blue dot)
Within 5ft - 10ft (Pink dot)	Within 15ft - 20ft (Light Blue dot)

ROW# _____
 Contractor _____
 Foreman Name _____
 Date Completed _____

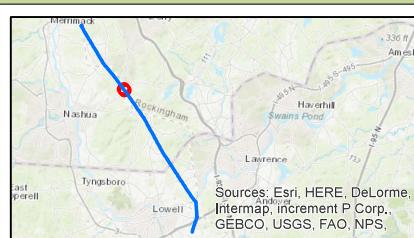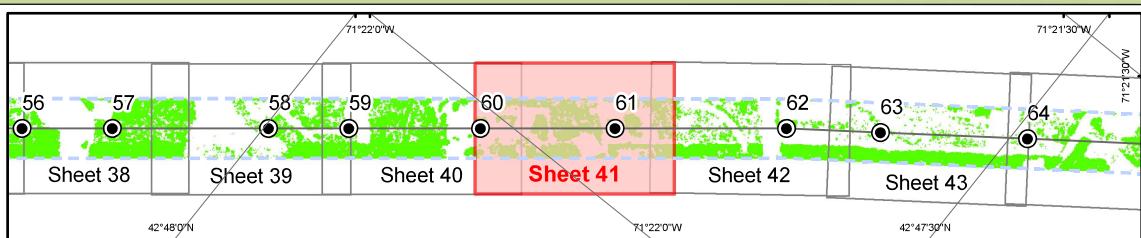

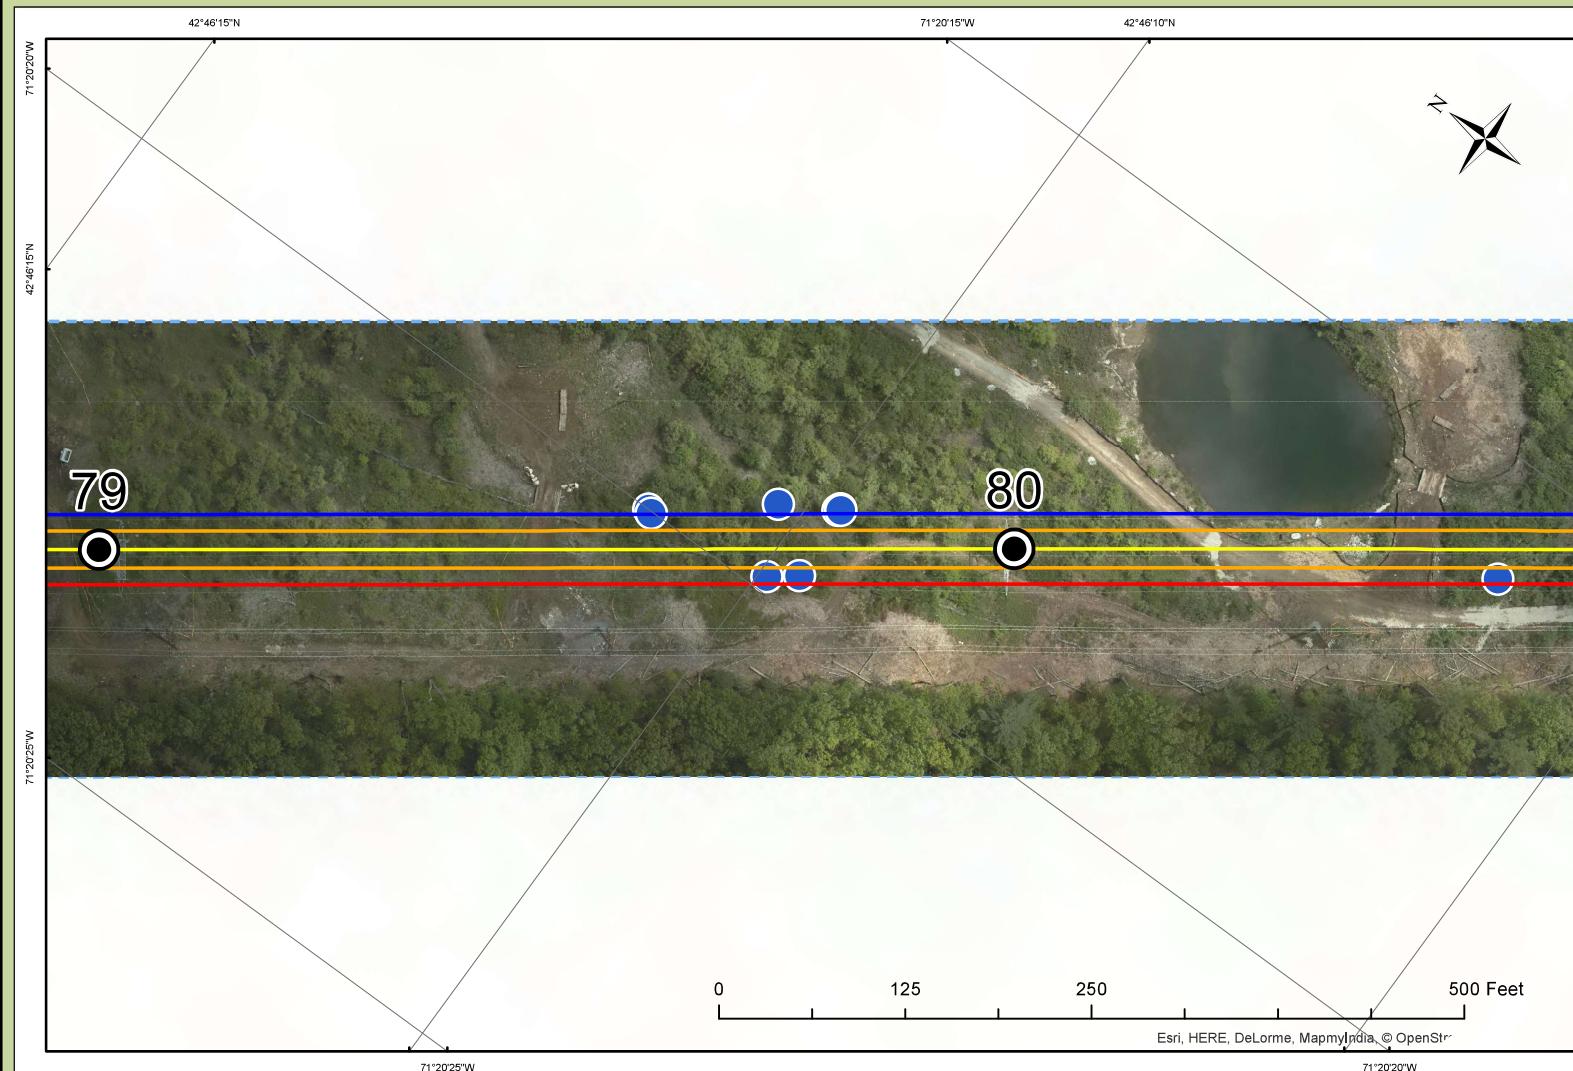

Title:	A3 VEGETATION CLEARANCE FIELD MAP	
Circuit:	O215	
Circuit Name:	North Litchfield - Tewksbury	
Sheet Number:	Sheet 55 of 125	
Project Ref.:	NMIP17053	
Coord. System:	UTM - NAD83	
Zone:	19 N	
Units:	US Feet	
Survey Date:	May 2017	
Version:	1.0	
Published Date:	12/09/2017	
Client:	National Grid	

Legend

-  Conductor Left
 -  Conductor Centre
 -  Conductor Right
 -  Shield Wire
 -  Right of Way
 -  Tower

Infringements 115kV lines: Infringements 200+kV lines:



- Within 5ft
 - Within 15ft
 - Within 5ft - 10ft
 - Within 15ft - 20ft

ROW#

Contractor

Foreman Name

Date Completed

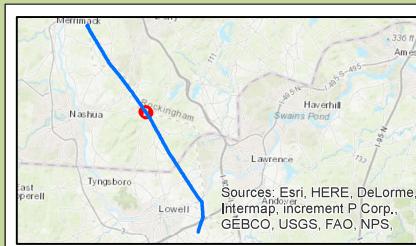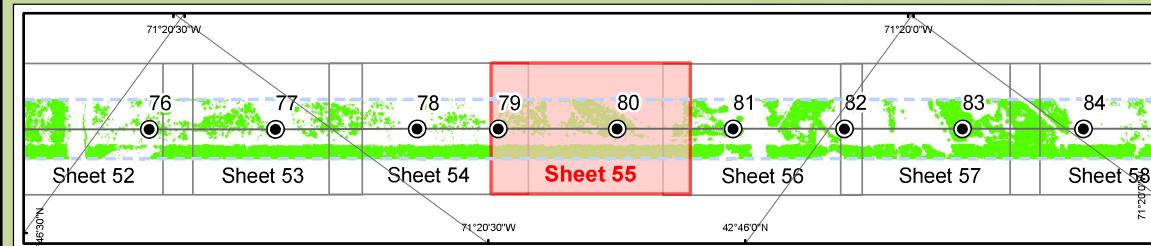

The logo for NM Group, a Trimble company. It features the word "NM" in large green letters, "Group" in smaller green letters to the right, and "A TRIMBLE COMPANY" in smaller black letters below. To the left is the "nationalgrid" logo in blue.